



STANDARD FEATURES	
ITEM	DESCRIPTION
01	PRV W/ 0.25 NPT COUPLING
02	OIL FILL/UPPER FILTER PRESS 1.0 NPT COUPLING
03	HV BUSHING WELL W/FIXED STUD (ELAST#L1601-PCS1)
04	LV BUSHING, (HJ# EPC10-090-029E01T01)
06	LIFTING LUGS X (4) WITH TIE-DOWN PROVISIONS
07	BOLTED COVER
08	SS 2-HOLE GROUND PADS
09	JACKING PROVISIONS
10	NAMEPLATE LASER-SCRIBED ANODIZED ALUMINUM
11	PAD MOUNTING PROVISION
12	1" NPT DRAIN VALVE W/ 3/8" SAMPLER (HJ#DV1000-001)
13	12" REMOVABLE SILL
14	PAD LOCKABLE DOOR HANDLE, PENTA-HEAD BOLT
16	REMOVABLE LV-HV BARRIER 3" FROM BASE
18	REMOVABLE TAMPER GUARD FOR COVER
22	TAP CHANGER
24	8-HOLE INTEGRAL SPADE
25	35KV LOADBREAK INSERT (ELAST#3701A3A)
27	OIL SAVER BOX
29	COOLING FINS
32	BOLTED CABINET COVER
33	FIXED CABINET SIDES
38	4-POSITION "T" BLADE SWITCH (CP#LS4RH3T12B)
39	WEAKLINK ABB 345B995G27 CURVE 9)
41	TEMPERATURE GAUGE
42	LIQUID LEVEL GAUGE
43	PRESSURE/VACUUM GAUGE
48	HO BUSHING

CUSTOMER APPROVAL	
FOR APPROVAL ☐	FOR RECORDS ☐
APPROVED AS IS _____	
APPROVED AS NOTED _____	
NOT APPROVED _____	
SEND SIGNED COPY TO : ERMCO ATTN: 3 PHASE SALES 2225 INDUSTRIAL RD. DYERSBURG , TN. 38025	


NOTES :	
1) ALL DIMENSIONS ARE IN INCHES UNLESS NOTED	
2) FILLED W/MINERAL OIL	
3) SECOND NP LOCATED INSIDE LV DOOR	
4) MUNSELL 7GY 3.29/1.5 PADMOUNT GREEN	

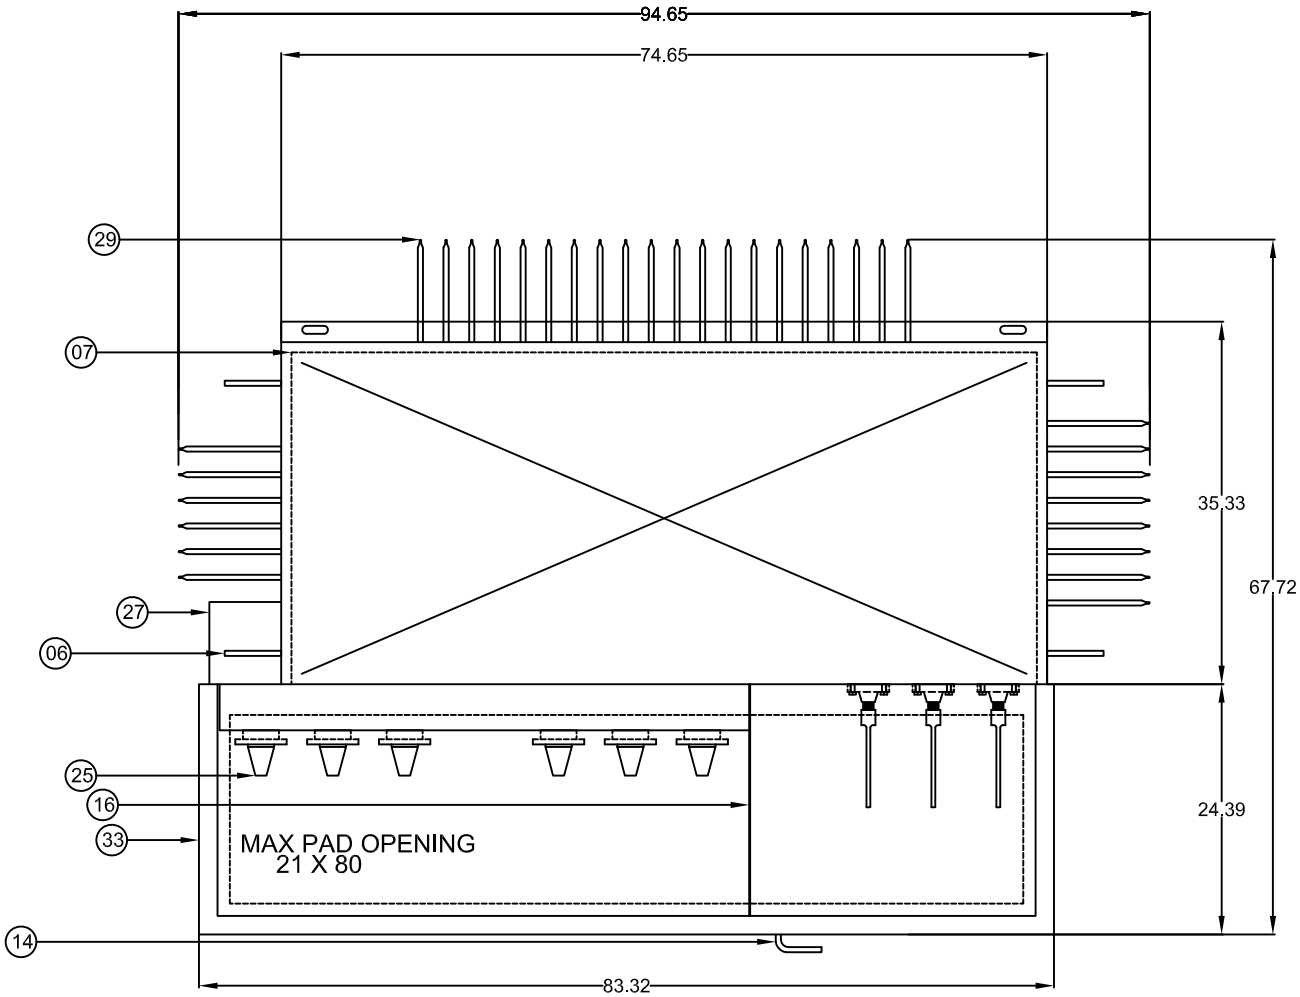

TOP VIEW WITH CABINET COVER REMOVED

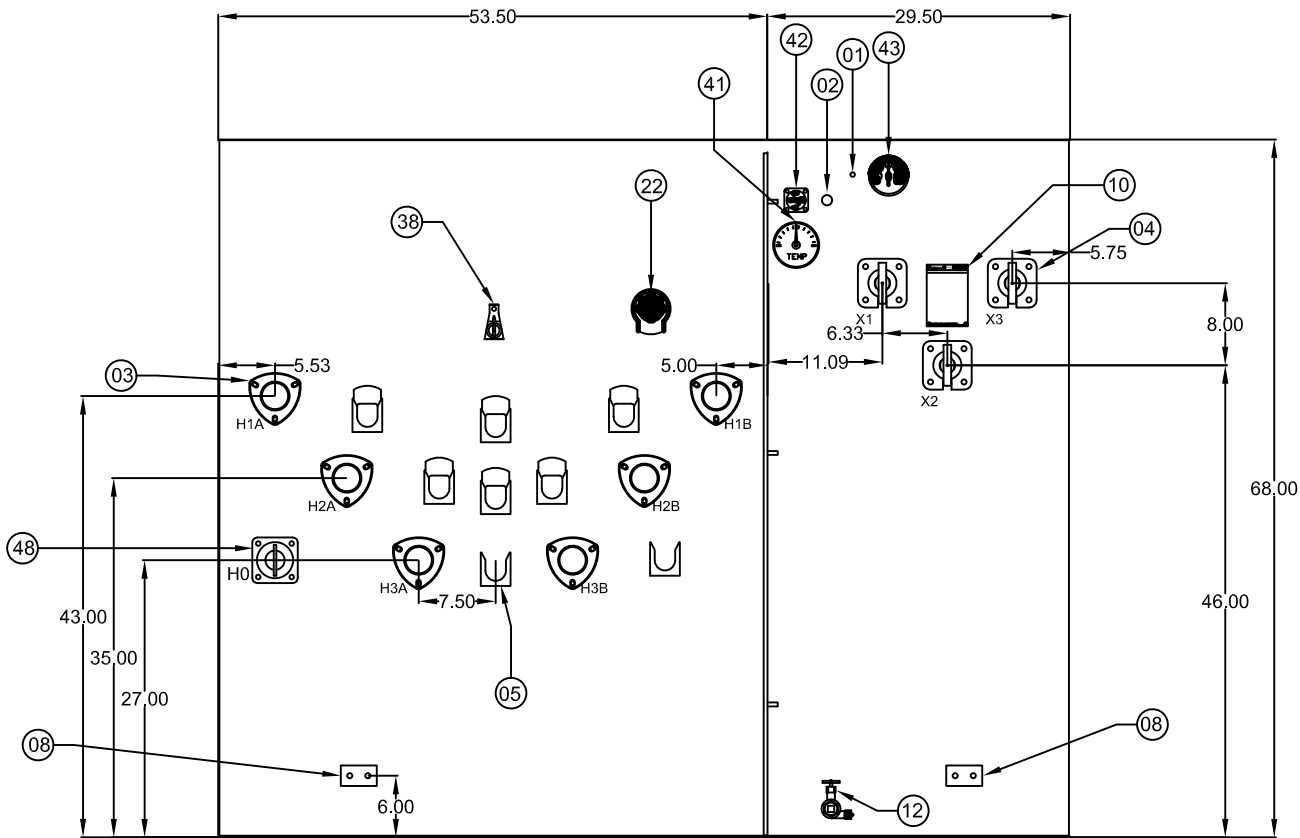

FRONT VIEW WITH CABINET REMOVED

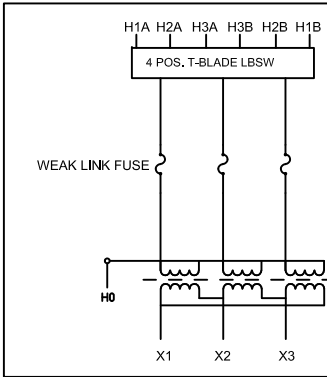

3 PHASE PAD OUTLINE

DWN BY: GY DATE: 12/23/19

ISSD BY: ER DATE: 12/23/19

PO #:

DWG NO. 561660.001

STOCK #:

CUSTOMER: MADDOX INDUSTRIAL TRANSFORMER

SPEC. DATED

KVA 2000

HIGH VOLTAGE 34500Y/19920

LOW VOLTAGE 600 DELTA

APPROX. CORE AND COIL WEIGHT 5819 LBS


APPROX. TANK AND ACCESS. WEIGHT 3490 LBS

GAL. OF OIL 534 APPROX.WEIGHT 4007 LBS

APPROX. TOTAL WEIGHT 13316 LBS

REV. DATE DESCRIPTION APP BY

SCALE: NTS

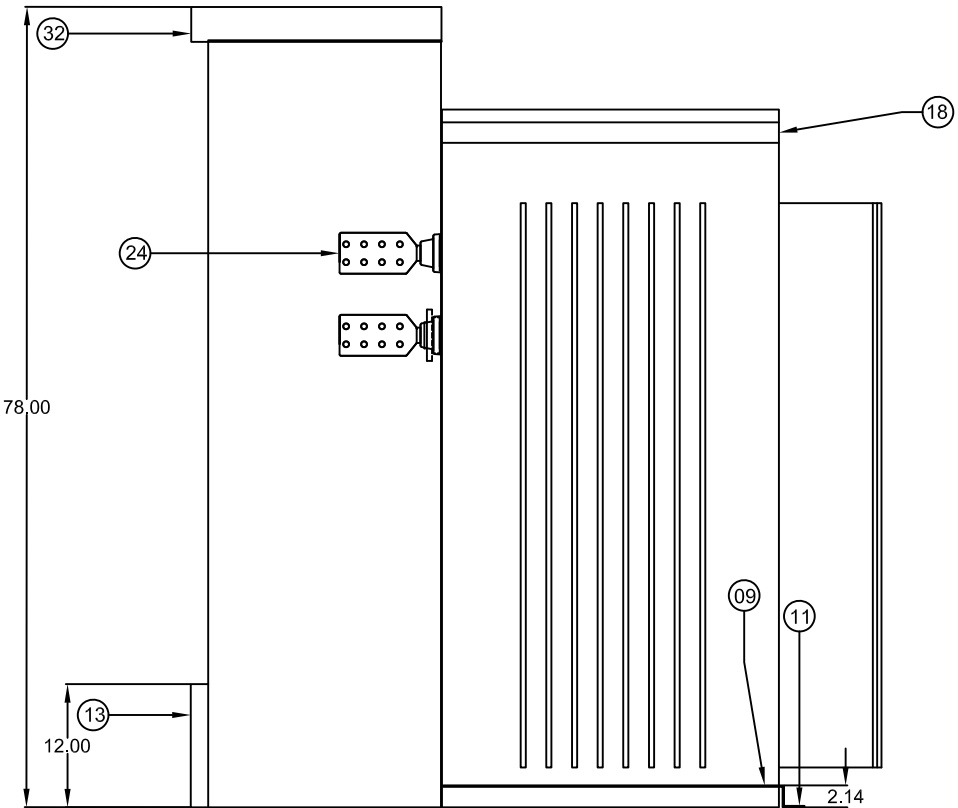

SIDE VIEW WITH CABINET DOORS AND SIDES REMOVED