

		DATE: 11-30-22	SUBMITTAL NO.: 33 73 13 – Padmount Liquid-Filled Utility Transformer	
To:		☐ This is a New submittal ☒ This is a Re-Submittal		
			Project Name: Port Heiden Distribution Upgrade Project	
Item Number	Description of Item Submitted	Number of Copies	Contract Reference Document	
			Spec Paragraph	Drawing Sheet #
33 73 13-1A3	Shop Drawings & Product Data – Transformers	Electronic	33 73 13/1.4/A/1	

Transformer testing testing shall include no load and full load losses. If losses exceed DOE standards transformers will be rejected.

CONSULTANT REVIEW ☐ DISAPPROVED ☐ APPROVED ☐ APPROVED AS NOTED ☐ RESUBMIT	
Comments:	
By: _____ Date: _____	


GENERAL CONTRACTOR REVIEW:

Reviewed By: _____
(Signature)

Wolverine Supply, Inc.
 Name: Bruce Van Buskirk
 Title: Project Manager
 Date: 12-1-22


I certify that the above submitted items have been reviewed in detail and are correct and in strict conformance with the contract drawings and specifications except as otherwise stated.

37.6" Length

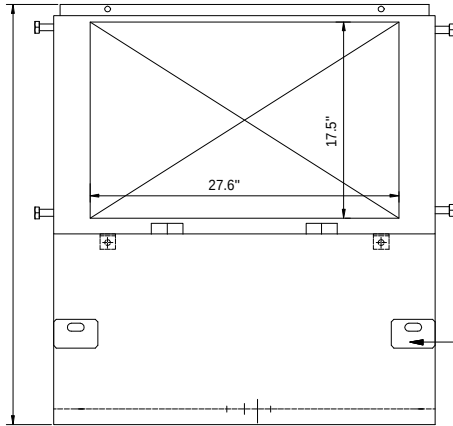

21

Diagram for connect

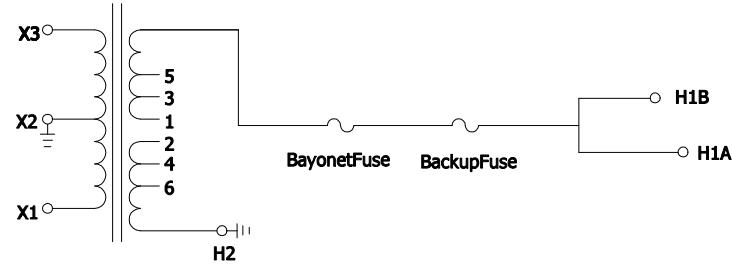

TECHNICAL DATA



RATING :	15kVA
PRIMARY VOLTAGE (V):	12470Y/7200
SECONDARY VOLTAGE (V):	240/120
FREQUENCY:	60Hz
VECTOR GROUP:	II0
WINDING MATERIAL:	ALUMINUM
EFFICIENCY:	98.82%
LOAD LOSS AT RATED VOLTAGE:	126.5w
NO LOAD LOSSES:	61w
IMPEDANCE :	3.5%
ALTITUDE :	1000m
No.OF TAP POSITION:	5 TAPS
COLOR :	Munsell 7GY3.29/1.5
core material:	Amorphous Alloy

ITEM	WEIGHT
TANK & ACCESSORIES	440 Pounds
TOTAL OIL WEIGHT	60 Gallon
TOTAL WEIGHT	1100 Pounds

size: Inch

PARTS LIST

ITEM	DESCRIPTION	QTY
1	304 stainless lifting bolt	4
2	304 stainless rain cover	1
3	bushing support	1
4	304 stainless tank, lid,hinges,locking mechanizing penta bolt	1
5	LV bushing(0.62-11UNC-2A)	3
6	equipotential device(inner)	1
7	oil fill plug	1
8	oil drain plug	1
9	grounding copper bar	1
10	HV bushing well	2
11	earth terminal	2
12	nameplate	1
13	hand pull value(pressure release value)	1
14	backup fuse	1
15	bayonet fuse	1
16	oil collection box	1
17	304 stainless fasten bolt assembly with haps for a paddle lock	1
18	oil level gauge	1
19	HV plug-in bushing(15KV,200A)	2
20	tap changer(WBPII-63/15-6X5QS)	1
21	transport fixed plate	2

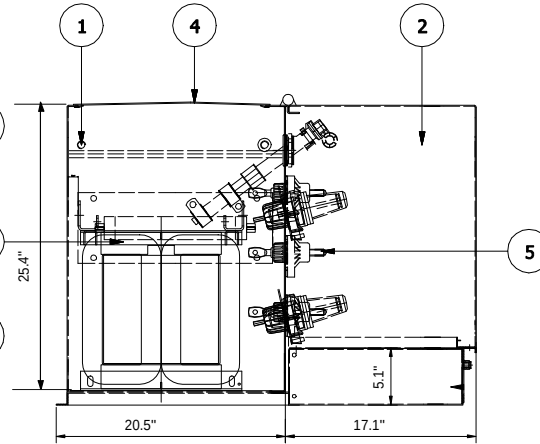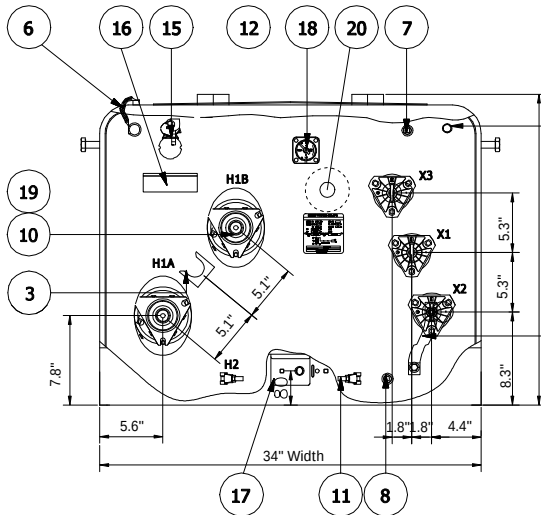

TYPE

ZGDL-H-15/7.2/0.24(0.12)

DWG. NAME

General Assembly Drawing

DRAWN

X.F.Ding

CHECKED

S.F.Zhou

CHECKED

A.H.Tong

APPROVED

B.Dong

FIRST ANGLE
PROJECTION

SCALE

1

REV.
NO.

0

1LD.710.22015